

**TECHNICAL DETAILS
LIVING SHELTER (06 MEN) IN HQ CIF (R)**

Ser No	Brief Description	Remarks
1.	Prefabricated Living Shelter of size 06.00 x 6.00 M clear ht 2.80 M at both sides and 3.20 M at the central gable with two PIR foam wall panel doors and six aluminium sliding windows mounted on MS Angle Iron Pedestal.	
2.	PIR FOAM WALL PANEL:- 2.1. PIR foam wall panels manufactured on continuous line production plant and should generally conform to IS 12436 of May 2002. 2.2. Thickness – 60mm 2.3.GI metal skin for Panels:- 2.3.1. Thickness – 0.5mm 2.3.2. Pre Painted GI Sheet – Conforming to IS 5965: 2012/ASTMA755 foam apvd supplier with max yield stress of 300N/mm², coated with aluminium- Zinc alloy coating AZ150 (150 gms/m²) and both side coated with silicon modified polyester paint coat (min 25 micron) 2.3.3. Inner Walls Panel Finish: Factory-finished ivory colored paint on all inner walls/as approved by the CO/EPO. 2.3.4. Base metal of GI skin CRCA as per IS-513 and galvanized as per GR-120, IS-277. 2.3.5. Density – 40+2 kg/m³ 2.3.6. K Value at 10 min temp – 0.0180W/MK 10 min temp (IS - 12436/IS- 6203/ASTMC518) 2.4. Closed Cell Content- 85% (min) 2.5. Resistance to fire – E115 (Integrity and insulation 15 min each) (BS476 Part-20 and 22) 2.6. Reaction to fire – B- S1d0 (BSEN 13501-1:2018) 2.7. Horizontal Burning Characteristics- Maximum 5mm 2.8. Green Material – 100% recyclable (CFC and HCFC free) 2.9. Locking Amg – Tongue and Groove	
3	Column (08 Nos): - 8 Nos MS Columns of rectangular section of size 96 x 48 x 3.2 mm thick with base plate and top plate of size 150x150x6mm with 4 No predrilled holes in each plate welded on top and bottom to pipe with 16mm dia 600mm long bolt with nuts and washer at bottom and 10mm dia 50mm long nuts and bolts with washer at top and all end clades complete. Make: TATA/SAIL/RINL/JINDAL or Equivalent to IS-4923:1997	
4.	Roof. The roof shall be in slope 1:4 approximately. 4.1. The roof shall be done with Pre-coated, pre-coloured, profiled sheet 0.60 mm thickness, camouflage colour. These profile sheets are laid over a frame work of trusses, columns and purlins fixed using self drilling screw with washers. A ridge cover of size 225 x 225 x 0.60 mm made from pre-coated, pre-coloured, profiled sheet is to be fixed on top junction of the roof using suitable fasteners. Pre- coated, pre-coloured profiled sheet in camouflage pattern to be used on external roofs surface. Make-TATA/JINDAL/SAIL/RINL or Equivalent to IS -277-2003 4.2. 2mm thick polycarbonate profile sheet, UV protected ER clear having similar profile as colour coated sheet of roof shall be provided for skylight, the skylight area will be 10% of total roof area. Make: Polaris, Ghyzod, PC shine or equivalent to IS 1361-1978	

RESTRICTED

Ser No	Brief Description	Remarks
5.	Non-asbestos fibre cement designer board False Ceiling: - 4 MM thick non-asbestos fibre cement designer board ISI marked fixed with screw to aluminium frame work in ceiling flat or sloppy mounted on anodised aluminium snap grid frame work for false ceiling for size of grid 605 x 605 MM including hangers 3MM dia GI (up to 1200 MM long) adjusting level fixed to roof complete all as specified as directed. The false ceiling panels are placed onto a suspended grid frame of size 600mmx600mm made of Aluminium 'L' & 'T' sections of 0.60 mm conforming to IS 2095 (Part 1): 2011. The false ceiling grid is suspended from the roof framework with the help of galvanized wire of 3.00mm dia. The finished clear height of the false ceiling shall be 2.80m from floor level.	
6.	Ridge. Ridge shall be provided with 0.60 mm thick pre coated, pre coloured plain sheet fixed with self tapping screws. Make- TATA/JINDAL/SAIL/RINL or Equivalent to IS -277-2003.	
7.	Roof Projection. The roof projection on the gable end and sides shall be 30 cm and 45 cm respectively.	
8.	Sunshades. 8.1. Sun shade 450 mm wide extended to 150 mm on either side of window to be fixed with Pre-coated pre-coloured (camouflage pattern) profile sheet 0.60mm thick fixed with self tapping screw to MS frame work. Sun shade shall be provided only on the rear & side windows only. 8.2. Sunshades should be fitted min 150mm above the top of the window.	
9.	PIR foam Wall Panel Door (02 Nos). The PIR foam wall panel door shall be of size 0.90 x 2.10 m, made in sandwich panel system using 02 Nos 0.55 mm thick zinc plated pre-coated, pre-coloured MS sheet with 40 mm gap for polyurethane foam fitted in the outer aluminium frame including lock with lever type handle on both sides' incl aluminium high grade fittings. PIR foam wall panel door with external as, camouflage and internal as teak finish to be used.	
10.	Aluminum Sliding Windows (06 Nos). The sliding aluminium windows with three channels of sliding to include two windows made of solid compact polycarbonate clear sheets of thickness 2mm UV protected, scratch proof (test certificate to be submitted by vendor with supply of material) and 01xwire mesh window shall be of size 1.2x1.00m. Make: TATA/SAIL/RINL/JINDAL or Equivalent to IS 1948-1961.	
11.	Fly Proofing Door (02 Nos). The aluminum door shall be of size 0.90 x 2.10 m made of fly proof mesh fitted in the outer aluminum frame including lock with lever type handle on both sides incl aluminum high grade fittings. Make: TATA/SAIL/RINL/JINDAL or Equivalent to IS 1948-1961.	
12.	Floor Boards. Floor board shall consist of MS frame of RHS 40 x 20 x 2 mm with 1 mm thick MS sheet on bottom and 2 mm thick aluminium chaqured sheet fused with PUF in between all chequered plate be wrapped around edges and sealing out joints with 40 mm wide and 1 mm thick aluminum strip fixed with anti rust screws.	
13.	MS Step (02 Nos). MS step shall be made of hollow RHS of size 50 x 25 x 2 mm of size 1.00 x 0.40 x 0.2 m with flat iron 25 x 5 mm welded vertical @ 25 mm c/c along longer span. Two additional intermediate support of angle iron 25 x 25 x 3 mm shall be provided along shorter span below flat iron.	
14.	Curtain/ Drapery Rod. 25mm dia drapery rod GI pipe 1.2 m long with colour powder coated alongwith 12 cotton rings with decorative both end sockets and brackets with complete fixing arrangement	
15.	Electrical Stores. The minimum electrification will be provided as per store list attached.	
16.	Earthing Material 16.1. Finished GI plate 600mmx600mmx6mm - 01 Nos 16.2. GI Wire 4 mm dia - 15 Mtr 16.3. Cast Iron cover of size 300 x 300 x 6 mm - 01 Nos with angle iron 30 x 30 x 6 mm frame with locking arrangement as Allen Key 16.4. Charcoal - 25 Kg 16.5. Common Salt - 25 Kg 16.6. GI pipe 20 mm dia, 2 m long - 01 Nos 16.7. Nut and bolts size No 12 - 04 Nos	

RESTRICTED

RESTRICTED

Ser No	Brief Description	Remarks
17.	Lightning Arrester System. Prefabricated gel earthing electrode of pipe in pipe technology. Two B class IS mild steel pipes, one inside the other, hot galvanized with 100-micron coating outside and about 300-micron coating dip inside, filled with high conductor and corrosion resistant crystalline mixture and back fill compound around electrode as per IS 3043/1987 as per Drawing att. 17.1. Earth Work. Excavation shall be carried out rocky soil for earthing pit of size 0.6 m x 0.6 mtr x 2.0 m depth including removal of surplus soil in low laying area. 17.2. Down Conductors. Aluminium strip size 25 mm x 3 mm of length 9m ISI marked. 17.3. Earthing Strip. Aluminium strip 32 mm x5 mm of length 3 m. Qty Nos 01 each. ISI marked. 17.4. Air Terminal. GI nipple 20mm dia and 10 cm length one copper ball having 05 Nos copper prong of 15 cm length. Prongs and nipple fitted to copper ball with threading arrangements ISI marked. Note Air terminal and down conductors should be fixed above ridge roof sheet/roof sheet(middle of the shelter) /out side wall panel & earth surface with suitable insulators and fixing arrangements.	
18.	Foundation for MS Angle Iron Pedestal. Four Nos foundation bolts of 16 mm dia 600 mm long to be embedded in PCC (1:2:4) block of size 300 x 300 x 750 mm for holding of MS angle iron pedestal welded with 6 mm thick MS plate welded on top and bottom over PCC 1:4:8 type D2 of size 400x400x75mm.	
19.	MS Angle Iron Pedestal. MS angle iron pedestal shall be made of 04 No MS angle iron legs of size 50 x 50 x 06 mm and height 0.30 m spacing 250 mm to form a square. MS plate 250 x 250 x 06 mm thick shall be welded on top and bottom. In addition diagonal cross bracing of MS square bar 12 mm to be provided on 04 sides. 04 No holes in the top and bottom plate shall be provided for fixing of columns/foundation bolt.	
20.	Rafter and Purlin. Rafter and purlin shall be of RHS 66 x 33 x 2.90 mm. 4 rows of rafter reinforced in the centre with 33x20x2.90mm MS rectangular pipe 0.90mtr long along shorter span and 06 rows of purlin along longer span shall be provided. Each rafter/purlin shall be welded at both ends with FI 40x60x100mm long 06 mm thick MS plate cleat and jointed with each other using Nut & Bolt. Make: TATA/SAIL/RINL/JINDAL or Equivalent to IS-4923:1997	
21.	PCC Brick Dwarf Wall. PCC Brick dwarf wall of size 230x550mm, 300mm above GL built in CM 1:6 will be provided on outer side of shelter in between columns over PCC 1:4:8 type D-2 of size 300x75mm complete all as shown in drg.	
22.	Plastering / Painting. 15mm thick rendering in CM 1:4 will be provided on outer side PCC brick wall including two coats of weather coat exterior emulsion over a coat of primer complete.	
23.	Furniture. The following furniture is required for the shelter:-	
	23.1. MS Cabinet (06 Nos). Cabinet of size 0.75 x 0.60 x 0.90 m with two partition, one partition with two shelf another partition with steel hanging rod incl shutter and fitting as shown in drgs. Thickness of MS sheet will be 1mm. Make: Godrej	
	23.2. Wooden Table (02 Nos). Pre-laminated particle board 25 mm thick teak finish table of size 1.40 x 0.70 x 0.75 m with drawers as shown in drawings.	
	23.3 MS single bunk bed (06 Nos). Steel single bunk made of MS square pipe 32mm 1.25mm thick with size 2050x900, with head board and foot board made out of 18x18mm MS square pipe 1.25mm thick and 18mm thick both side prelaminated particle board screwed to MS strip ARC welded to 18 mm thick rectangular pipe, PVC edging. Platform with 12 mm thick BWR phenol bonded commercial ply with edging. Plateform with 12 mm thick BWR phenol bonded commercial ply edging (unpolished) placed on top 25x25mm supports Make: KITPLY/ GREENPLY/ NATIONAL or Equivalent to IS- 303:1975 including good quality of cushion not less than 75 mm thick covered with good quality 350 gsm tarpaulin cover in OG colour with 16 mm hollow box bracing. One set of frame mosquitos net made of MS pipe should be provided as per Drg.	

RESTRICTED

Ser No	Brief Description	Remarks
	23.4. Plastic Chair:- Plastic Chair with arms. Make: Supreme/Cello/Nilkamal or Equivalent to IS 13713-1993.	
24.	Cloth drying fixtures: 24.1. Main vertical MS Angle of size 60x60x6mm of 2.4 mtr length (1.8 Mtr above ground level + 0.6 Mtr below ground level with PCC 1:3:6 of size 0.3x0.3x0.6Mtr. As per Drawing att. 24.2. Horizontal MS Angle of size 60x60x6mm of 1.2 mtr length fixing with (Welded) top and 0.3 mtr length fixing with bottom. 24.3. 04 x Nos galvanised Iron wire dia 3 mm length of each 8 mtr tied with Horizontal MS Angle.	


STORE LIST/ BRIEF DESCRIPTION
LIVING SHELTER (06 MEN) (04 NOS) IN HQ CIF (R)

Item S No	Items Title	Items Description	A/U	Qty
1	Prefabricated Living Shelter 6 Men	<u>LIVING SHELTER (06 MEN).</u> Prefabricated Living Shelter of size 6.00 x 6.00 M clear ht 2.80 M at both sides and 3.20 M at the central gable with two PIR panel doors and six aluminium sliding windows mounted on MS Angle Iron Pedestal including roofing, base, frame work, flooring, sun shades and MS Steps with 4 mm thick non-asbestos fibre cement designer board false ceiling panel along with anodised aluminum snap grid frame work with suitable 'T' and 'L' section. The false ceiling panels are placed onto a suspended from the roof frame work with the help of galvanized wire of 3.00mm dia. The finished clear height of the false ceiling shall be 2.80m. The finished clear height of the false ceiling shall be 2.80 m. (Cost of structure) complete as per drawing and specification. Make : TATA/JINDAL/ SAIL/ RINL or Equivalent to IS 808 (1989)	Nos	4
2	Ceiling Fan 1400mm	(a) Ceiling fan 1400 mm sweep with mini fan regulator. Make : USHA / ORIENT / KHAITAN or Equivalent to IS -374/1979	Nos	24
3	LED Panel Ceiling Lidht	(b) LED panel ceiling light 2'x2' recess type, 36 W 90-230V, 50 Hz , 3000 lumen, 50000 Hours life . Make:- HAVELLS/PHILIPS /SYSKA or Equivalent to IS - 16102	Nos	16
4	LED Tube Light Fittings 20W	(c) LED Tube light fittings 20W, 4 feet long complete in PVC sheathed wire of length 0.5 m for connecting to ceiling rose, Make:- BAJAJ/ HAVELLS/ PHILIPS/SYSKA/GOLDWYN or Equivalent to IS - 16102	Nos	8
5	Switch Socket combination 5 Amp 5 Pin	(d) Switch Socket combination 5 Amp 5 pin. MAKE:- HAVELLS/ANCHOR BY PANASONIC/LEGRAND or Equivalent to IS - 3854/1997	Nos	24
6	Switch Socket combination 15 Amp 5 Pin	(e) Switch Socket combination 15 Amp 5 pin. MAKE:- HAVELLS/ANCHOR BY PANASONIC /LEGRAND or Equivalent to IS -3854/1997	Nos	4
7	Piano type Switch 6 Amp	(f) Piano type Switch 6 Amp. MAKE:-HAVELLS/ ANCHOR BY PANASONIC /LEGRAND or Equivalent to IS -3854/1997	Nos	48
8	Rectangular PVC Switch Board	(g) Rectangular PVC Switch Board of size 10" x 12". MAKE:- HAVELLS/ ANCHOR BY PANASONIC / LEGRAND or Equivalent to IS -3854/1997	Nos	16
9	MCB DB Steel Sheet	(h) MCB DB made of steel sheet, phosphatised powder painted, with bus bar, neutral link, earth bar and DIN rail, 6 ways, single pole neutral, single door. MAKE : L&T/ LEGRAND/HAVELLS or Equivalent to IS/IEC -60898-1(2002)	Nos	4
10	FR Insulation tape	(j) FR insulation tape of size 9mx108cmx0.125 mm thick. Make: STEELGRIP/ STANDARED or Equivalent to IS -2448-1 (1963)	Roll	12
11	MCB 6 AMP	(k) MCB 6 AMP SP. MAKE : L&T/ LEGRAND/HAVELLS or Equivalent to IS/IEC - 60898-1(2002)	Nos	12

12	MCB 10 AMP	(l) MCB 10 AMP SP. MAKE : L&T/ LEGRAND/HAVELLS or Equivalent to IS/IEC - 60898-1(2002)	Nos	4
13	MCB 25 AMP	(m) MCB 25 AMP SPN. MAKE : L&T/ LEGRAND/HAVELLS or Equivalent to IS/IEC - 60898-1(2002)	Nos	4
14	PVC casing capping 25mm	(n) PVC casing capping 25 mm (ISI marked). MAKE : AKG/ PRESSIST or Equivalent to IS -14927-2 (2001)	RM	280
15	Black Screws 4mm x 19mm	(o) Black screws 4mmx19mm, in 100 Nos packet	Pkt	12
16	Black Screws 6mm x 40mm	(p) Black screws 6mm x 40 mm, in 100 Nos packet	Pkt	12
17	20 Watt Bulk Head	(q) 20 Watt Bulk Head fitting. Make:- HAVELLS/ PHILIPS/SYSKA or Equivalent to IS -16102	Nos	8
18	PVC Insulated cable copper conductor 1 point 5 Sqmm	(r) PVC insulated cable copper conductor 1.5 Sqmm (90 mtr roll) . MAKE:- HAVELLS/ POLYCAB/ FINOLEX or Equivalent to IS -732/1989	Roll	10
19	PVC Insulated cable copper conductor 2 point 5 Sqmm	(s) PVC insulated cable copper conductor 2.5 Sqmm. Make: HAVELLS/FINOLEX/POLYCAB or Equivalent to IS -732/1989	Roll	4
20	Ceiling Rose 6 Amp	(t) Ceiling Rose 6 Amp, 2 plate MAKE:- HAVELLS/ANCHOR BY PANASONIC /LEGRAND or Equivalent to IS -3854/1997	Nos	8
21	Main Switch 32 Amp	(u) Main switch 32 AMP, 240V, SPN in two way sheet steel enclosure. MAKE:- HAVELLS/ ANCHOR BY PANASONIC /LEGRAND or Equivalent to IS/IEC -60898-1(2002)	Nos	4
22	Change over Switch 32 Amp	(v) Change over Switch 32 Amp, 240 V, 50 Hz, DP. MAKE:- HAVELLS/ANCHOR BY PANASONIC /LEGRANDR or Equivalent to IS/IEC -60898-1(2002)	Nos	4
23	PVC Square Box	(w) PVC Square Box 4"X4". MAKE:- HAVELLS/ ANCHOR BY PANASONIC /LEGRAND or Equivalent to IS -3854/1997	Nos	24
24	PVC innersheathed unarmed Cable 10Sqmm	(x) PVC Innersheathed unarmed cable 10 sqmm Two core, 1100 V aluminium conductor MAKE:- HAVELLS/POLYCAB/FINOLEX or Equivalent to IS -732/1989	RM	128
25	Earthing Material	(y) <u>Earthing Material.</u> (i) Finished GI Plate 600mm x 600mm x 6mm thick - 01 Nos. (ii) GI wire 4 mm dia - 15 m. (iii) Cast Iron cover of size 300 x 300 x 6 mm with angle iron 30 x 30 x 6 mm frame with locking arrangement as Allen Key - 01 Nos. (iv) Charcoal - 25 Kg. (v) Common Salt - 25 Kg. (vi) GI Pipe 20 mm dia, 2 m long - 01 Nos	Set	4


26	Lightening Arrestor System	Lightening Arrestor System. Prefabricated gel earthing electrode of pipe in pipe technology. Two B class MS pipes one inside the other, hot dip galvanized with 100 micron thick coating outside and above 300 micron thick coating inside, filled with high conductor and corrosion resistant crystalline mixture and back fill compound all around the electrode. Conforming to IS-3043/1987 including the following:- (a) Air termination, single pointed, copper rod 12mm dia and 300mm long - 01 Nos (b) GI Pipe 100mm dia, 2.00 m long medium grade with base plate ISI Marked, Make: Jindal/Bansal/Surya or equivalent to IS 1239 -01 Nos (c) Back fill compound - 01 Bag (d) CI manhole cover of size 30cm x 30 cm with Handles- 01 Nos (e) Aluminium strip 25 x 3 mm, RM -09 (f) GI Strip 32 x 6 mm, RM -03. (g) Insulator for fixing down conductors as per relevant IS - 25 Nos	Set	4
27	Looking Mirror with plastic decorative frame	Hardware Items. (a) Looking mirror 1200x750x3.5mm thick with plastic decorative frame. Make: MODIGUARD/ SAINT GOBIN or Equivalent to IS 3438:1994.	No	8
28	Chromium Plated Peg table	(b) Chromium plated peg set of 6	Nos	24
29	MS Hook for ceiling Fan	(c) MS Hook for ceiling fan	Nos	24
30	25 mm Drapery Rod	(e) 25 mm dia drapery rod decorative with both end sockets and brackets 1.05 m long	Set	32
31	6mm Screw 100 mm long	(f) 6mm screw 100 mm long	Pkt	12
32	MS Cabinet with Two partition	Furniture. (a) MS Cabinet (06 Nos). Cabinet of size 0.75 x 0.60 x 0.95 m with two partition, one partition with two shelf another partition with steel hanging rod incl shutter and fitting as shown in drgs. Thickness of MS sheet will be 1mm Make : Godrej	Nos	24
33	Wooden Table prelaminate particle board	(b) Wooden Table (02 Nos). Pre-laminated particle board 25 mm thick teak finish table of size 1.40 x 0.70 x 0.75 m with drawers	Nos	8
34	MS Single Bunk Bed	(c) MS Single bunk bed :Steel single bunk bed made of MS square pipe 32 mm x 1.257mm with size 2050x900, with head board and foot board made out of 18x18 mm MS square pipe 1.257mm and 18 mm thick both side prelaminate particle board screwed to MS strip ARC welded to 18 mm thick rectangular pipe, with PVC edging. platform with 12 mm thick BWR phenol bonded commercial ply with edging (Unpolished) placed on top of 25x25 mm supports Make: KITPLY/GREENPLY / NATIONAL or Equivalent to IS 303:1975 including good quality of cushion not less than 75 mm thick covered with good quality 350 gsm tarpaulin cover in OG colour. One set of frame mosquitos net made of MS pipe should be provided as per Drg.	Nos	24
35	Plastic Chair with Arms	(d) Plastic Chair :-Plastic Chair with arms. Make : Supreme/Cello/Nilkamal or Equivalent to IS 13713-1993.	Nos	24

36	Non asbestos Fibre Cement Designer Board for False Ceiling	Non-asbestos fibre cement designer board False Ceiling: - 4 MM thick non-asbestos fibre cement designer board ISI marked fixed with screw to aluminium frame work in ceiling flat or sloppy mounted on anodised aluminium snap grid frame work for false ceiling for size of grid 605 x 605 MM including hangers 3MM dia GI (up to 1200 MM long) adjusting level fixed to roof complete all as specified as directed. The false ceiling panels are placed onto a suspended grid frame of size 600mmx600mm made of Aluminium 'L' & 'T' sections of 0.60 mm conforming to IS 2095 (Part 1): 2011. The false ceiling grid is suspended from the roof framework with the help of galvanized wire of 3.00mm dia. The finished clear height of the false ceiling shall be 2.80m from floor level.	Sqm	432
37	Main Vertical MS Angle	Main vertical MS Angle of size 60x60x6mm of 2.4 mtr length (1.8 Mtr above ground level + 0.6 Mtr below ground level with PCC 1:3:6 of size 0.3x0.3x0.6Mtr. As per Drawing att.	Nos	8
38	Horizontal MS Angle	Horizontal MS Angle of size 60x60x6mm of 1.2 mtr length fixing with (Welded) top and 0.3 mtr length fixing with bottom.	Nos	8
39	Galvanised Iron Wire dia 3mm length	04 x Nos galvanised Iron wire dia 3 mm length of each 8 mtr tied with Horizontal MS Angle.	RM	140

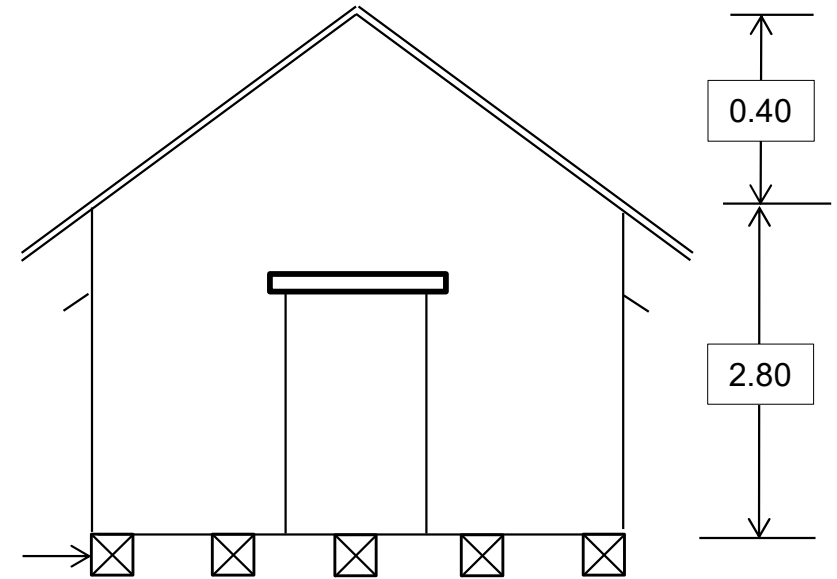


FRONT ELEVATION

LIVING SHELTER (06 MEN)	
JOB NO : OT/NC/16/CIF(R)/2026-27/6616	
SCALE : NTS	SHEET NO : 01/09
DATE : 2026	UNIT : 8 ENGR REGT
EPO	CO

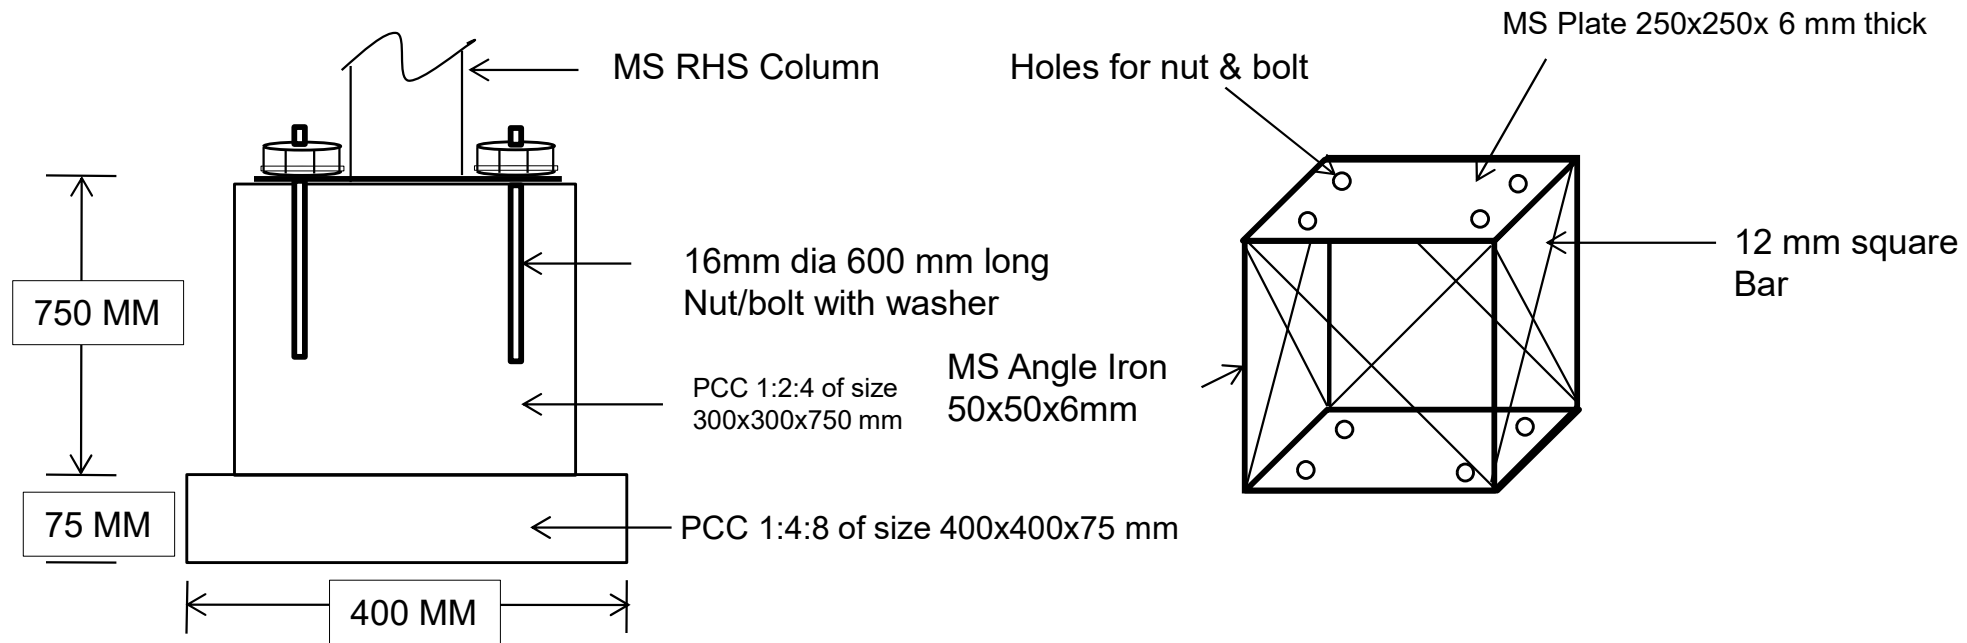


FOUNDATION DETAIL OF COLUMN

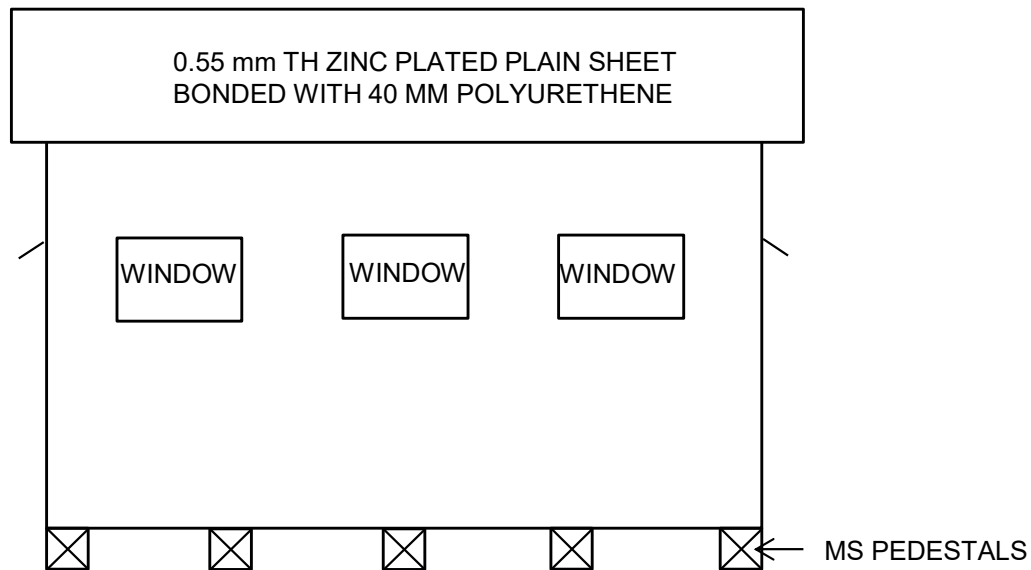

SIDE VIEW

LIVING SHELTER (06 MEN)	
JOB NO : OT/NC/16/CIF(R)/2026-27/6616	
SCALE : NTS	SHEET NO : 01/09
DATE : 2026	UNIT : 8 ENGR REGT
EPO	CO


CLOTH DRYING ARRANGEMENTS (MS CHANNEL & GI WIRE)

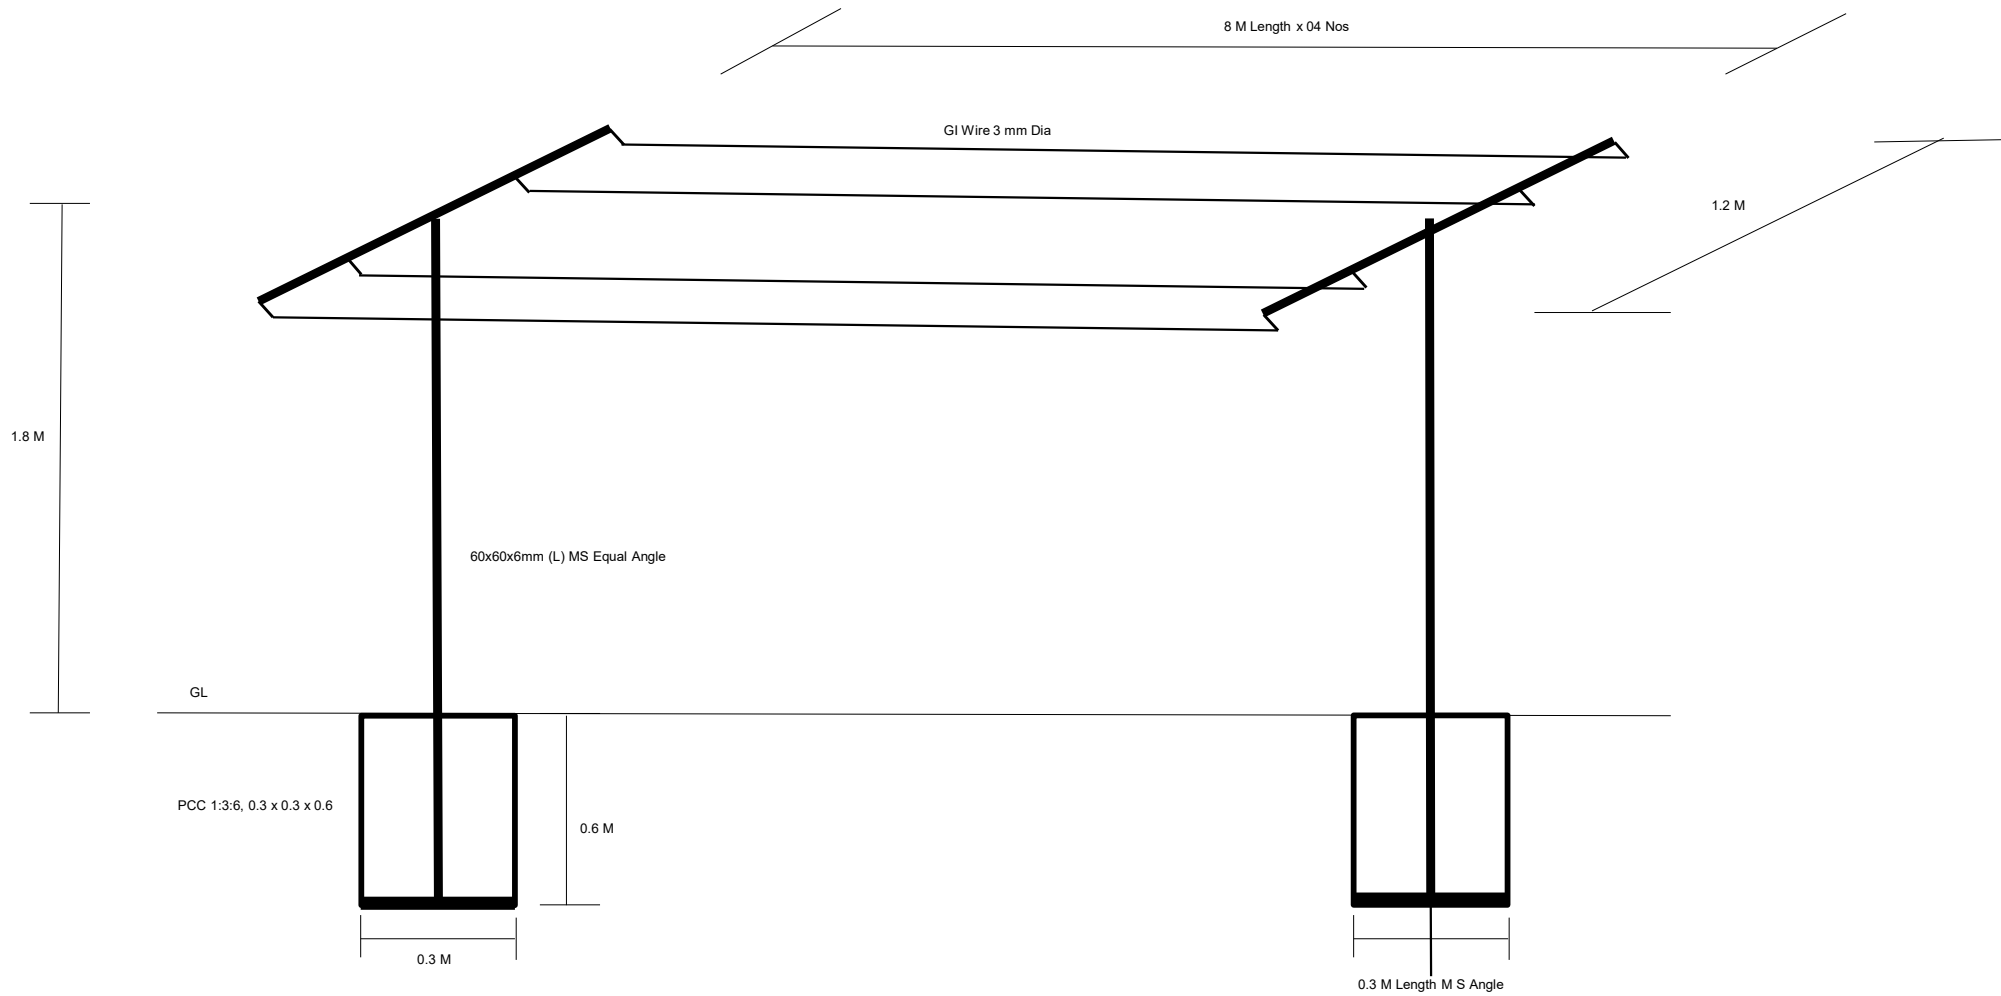

The diagram illustrates a lightning conductor system for a living shelter. It shows a cross-section of the shelter's roof and walls, with a lightning conductor strip running along the ridge. The strip is labeled "ALUMINUM STRIP 25 X 3 MM". At the peak, a "COPPER BALL WITH FIVE PRONG" is attached to a "GI NIPPLE & GI REDUSER SOCKET". The strip is connected to a "GI Strip 32 x 6 mm" that runs down the wall. The wall is made of "BRICK MASONRY WALL" and has a "50 Ø SLEEVE" for the strip to pass through. The strip is connected to a "HANDLE" and a "CEMENT CONCRETE" base. The base is labeled "CORROSION RESISTANT CRYSTALLINE MIXTURE". The diagram also shows a "CHARGE DISSIPATION BACK FILL COMPOUND MIXED WITH SOIL" around the strip. The outer pipe has a diameter of 100mm, and the inner pipe has a diameter of 40mm. The total height of the system is 2000mm. The diagram is titled "LIGHTNING CONDUCTOR" and "LIVING SHELTER (06 MEN)".


LIVING SHELTER (06 MEN)	
JOB NO : OT/NC/16/CIF(R)/2026-27/6616	
SCALE : NTS	SHEET NO : 01/09
DATE : 2026	UNIT : 8 ENGR REGT
EPO	CO

LIVING SHELTER (06 MEN)

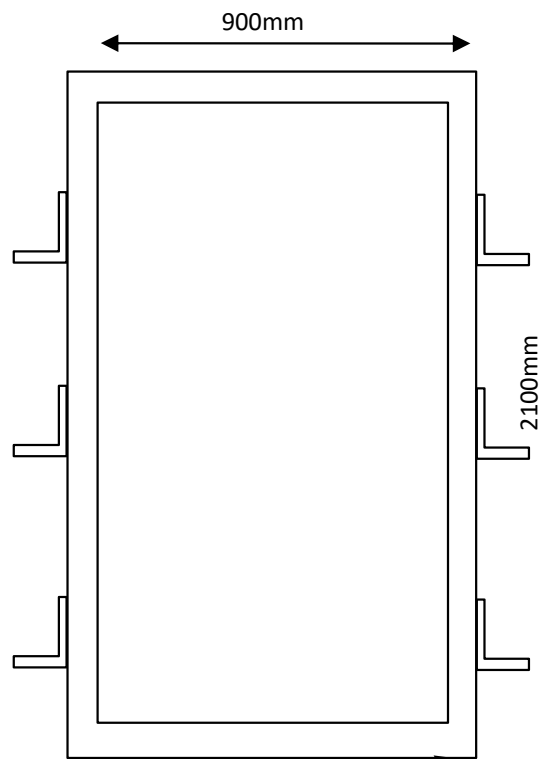


DOOR CHOWKAT


Aluminium frame

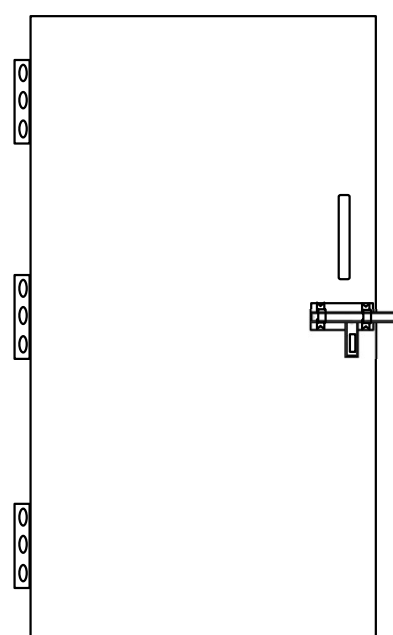

DOOR

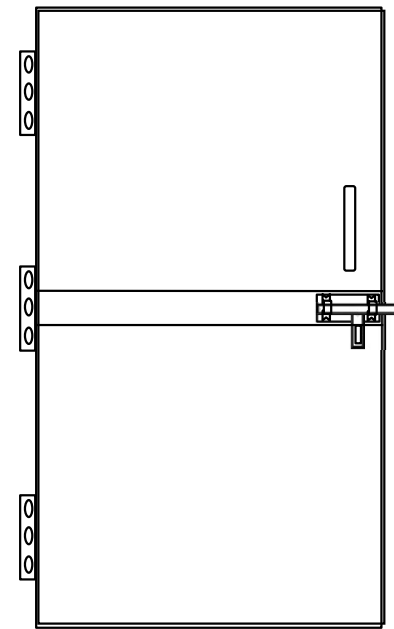

FLY PRROFING

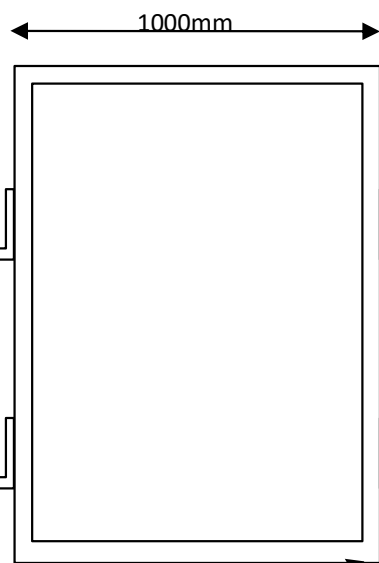


WINDOW FRAME



Aluminium frame

Aluminium Grill

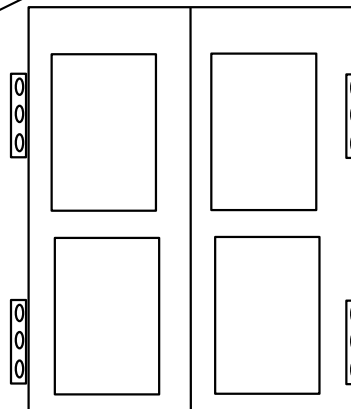

LIVING SHELTER (06 MEN)

JOB NO : OT/NC/16/CIF(R)/2026-27/6616

SCALE : NTS


SHEET NO : 01/09

DATE : 2026


UNIT : 8 ENGR REGT

EPO

CO

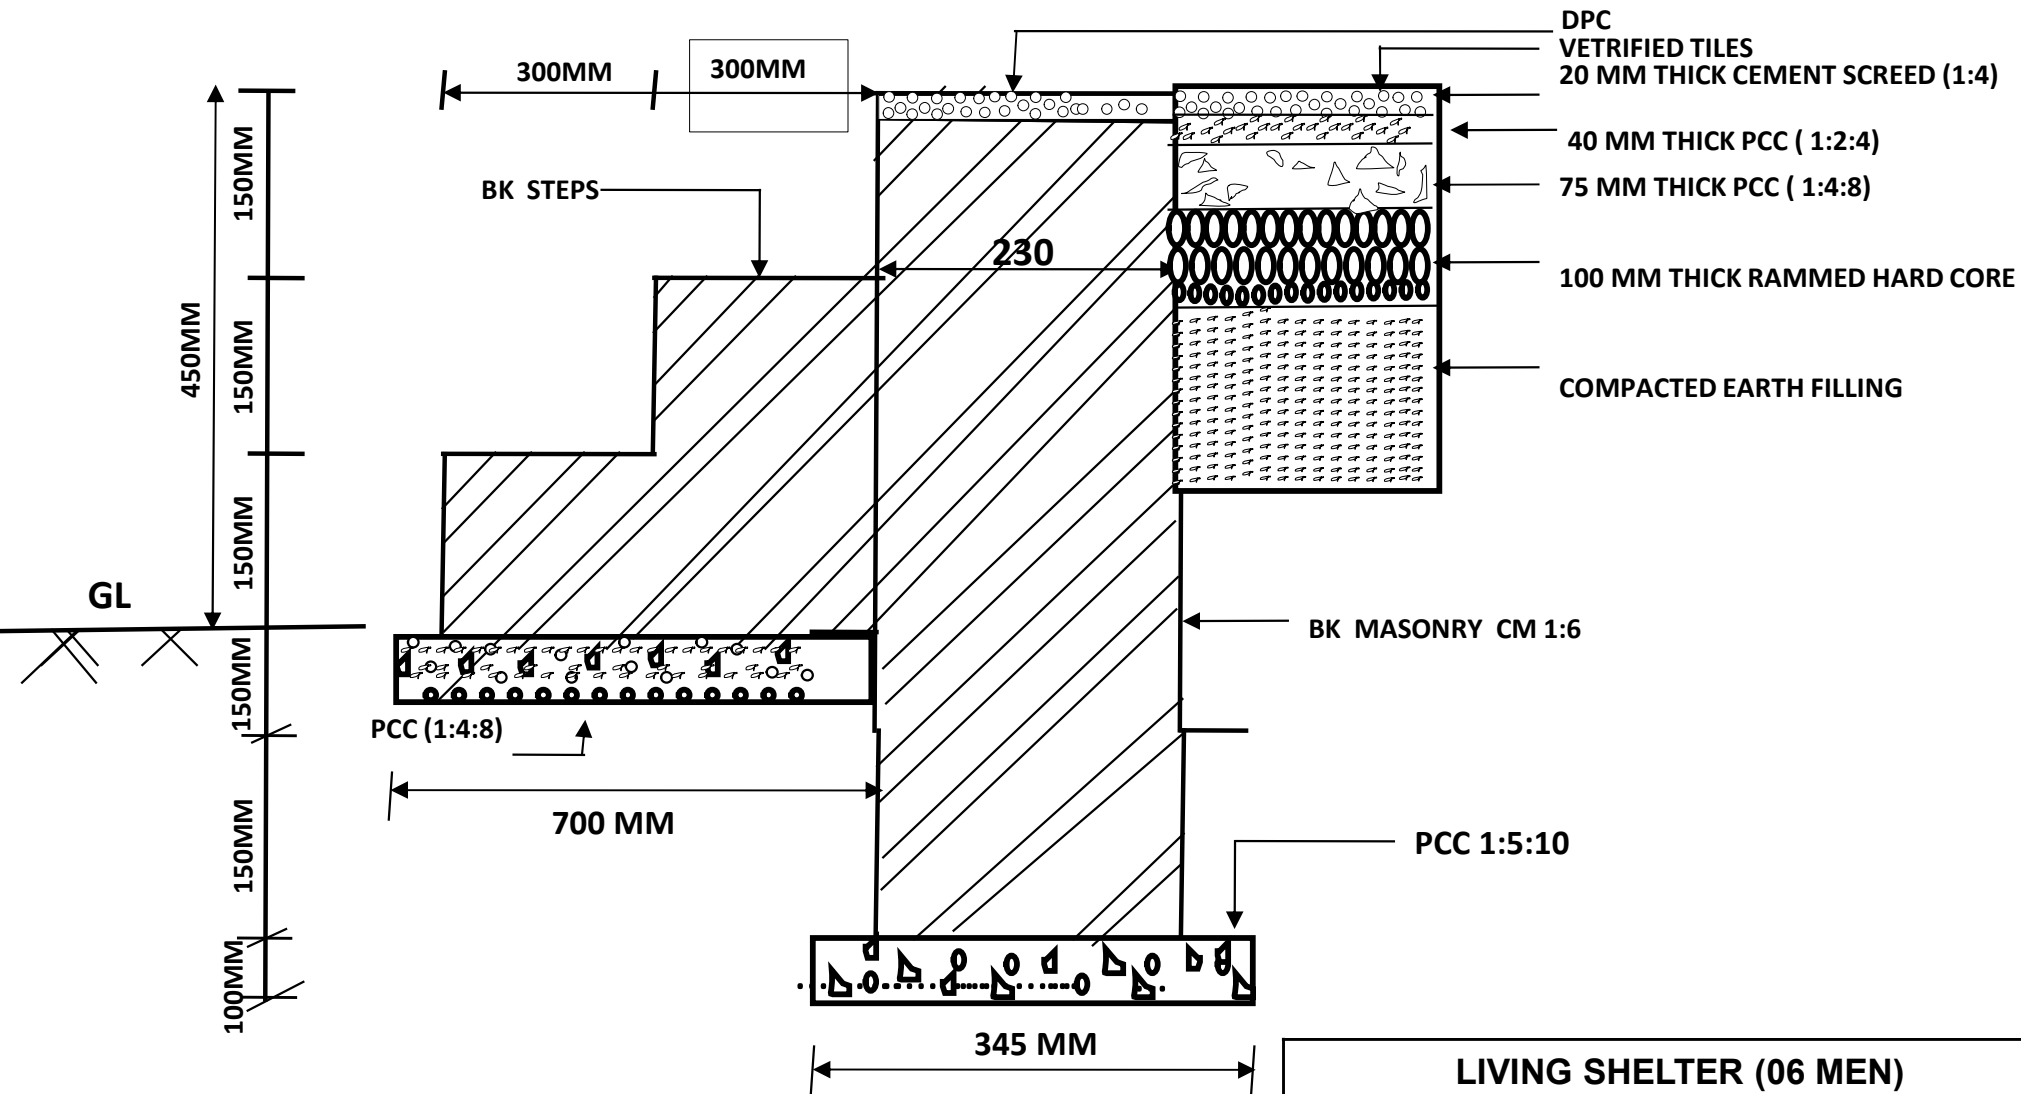


LIVING SHELTER (06 MEN)	
JOB NO : OT/NC/16/CIF(R)/2026-27/6616	
SCALE : NTS	SHEET NO : 01/09
DATE : 2026	UNIT : 8 ENGR REGT
EPO	CO

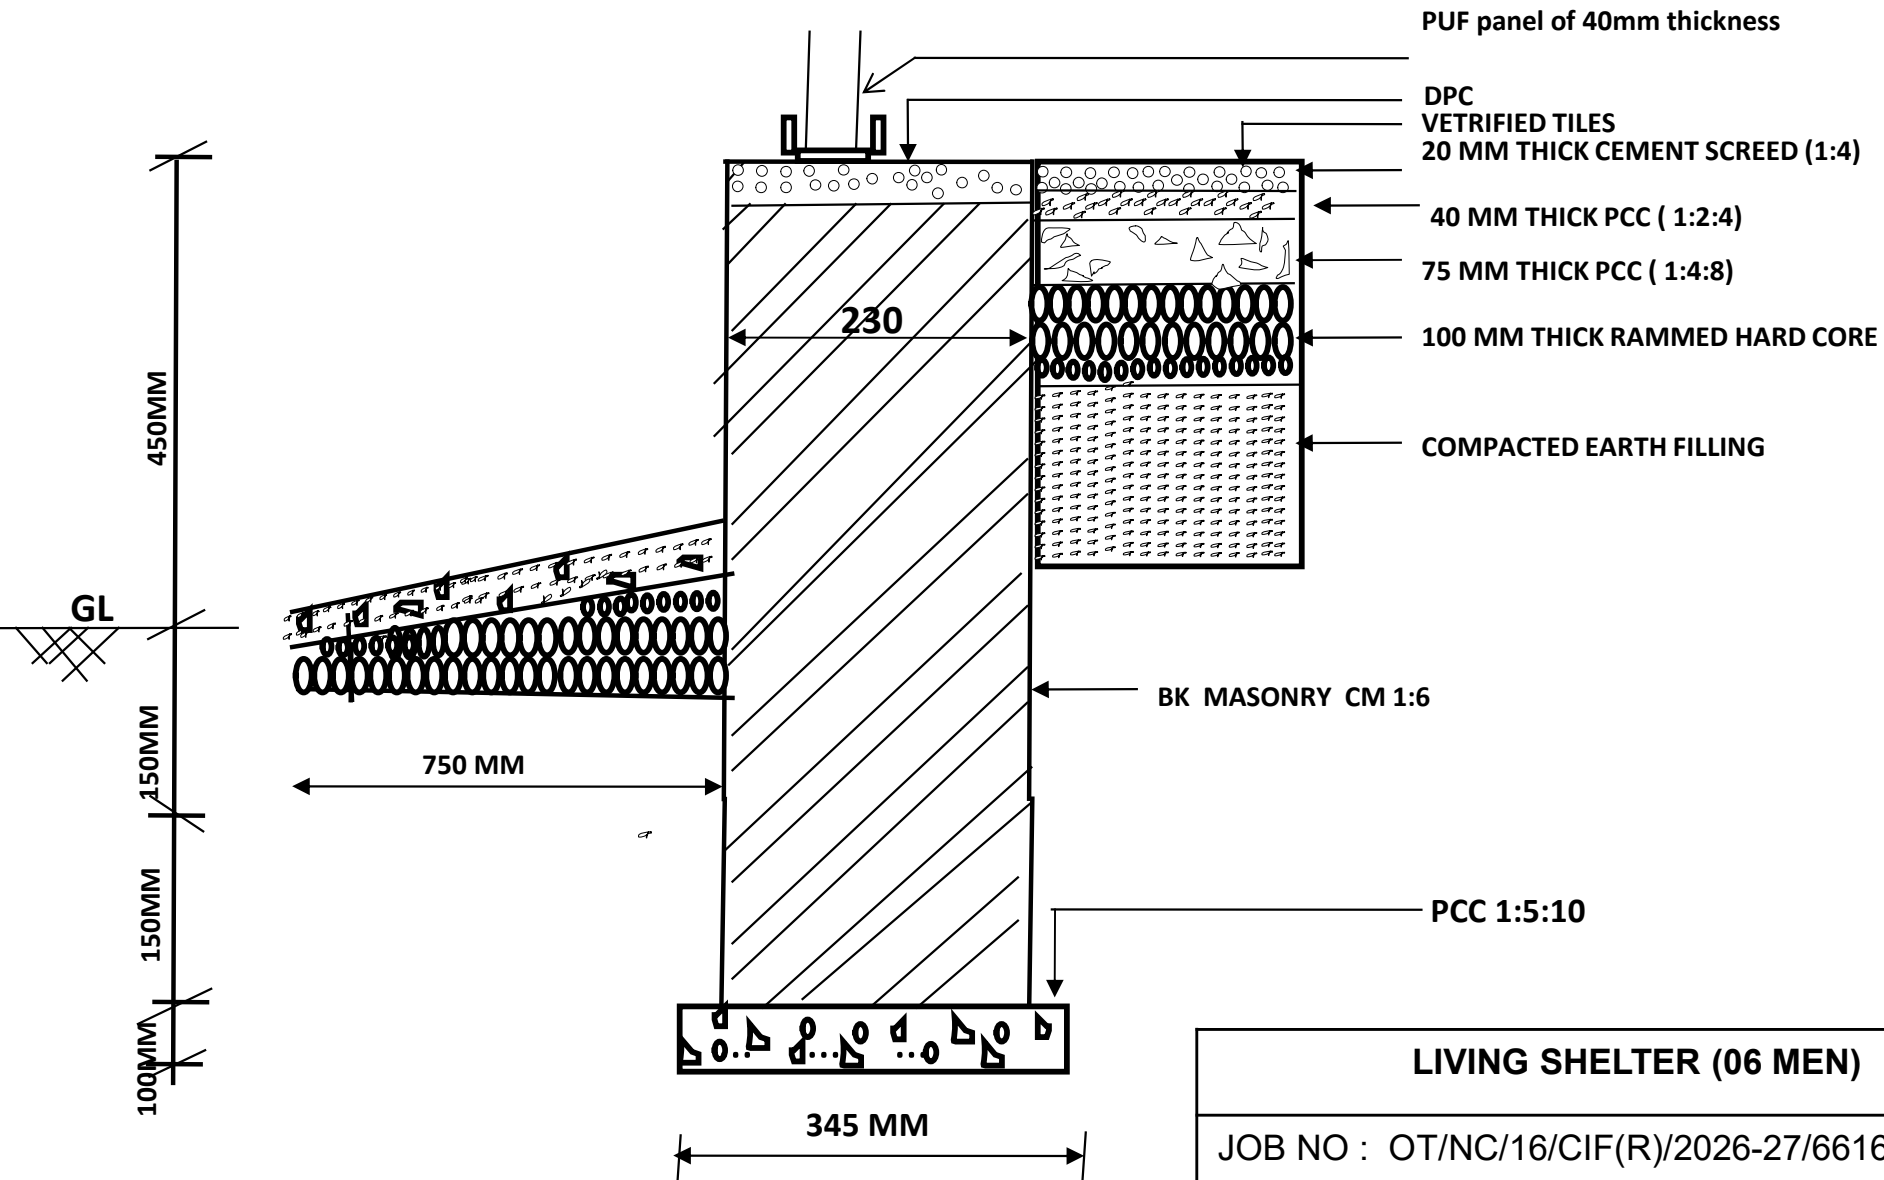


LIVING SHELTER (06 MEN)	
JOB NO : OT/NC/16/CIF(R)/2026-27/6616	
SCALE : NTS	SHEET NO : 01/09
DATE : 2026	UNIT : 8 ENGR REGT
EPO	CO

LIVING SHELTER (06 MEN)

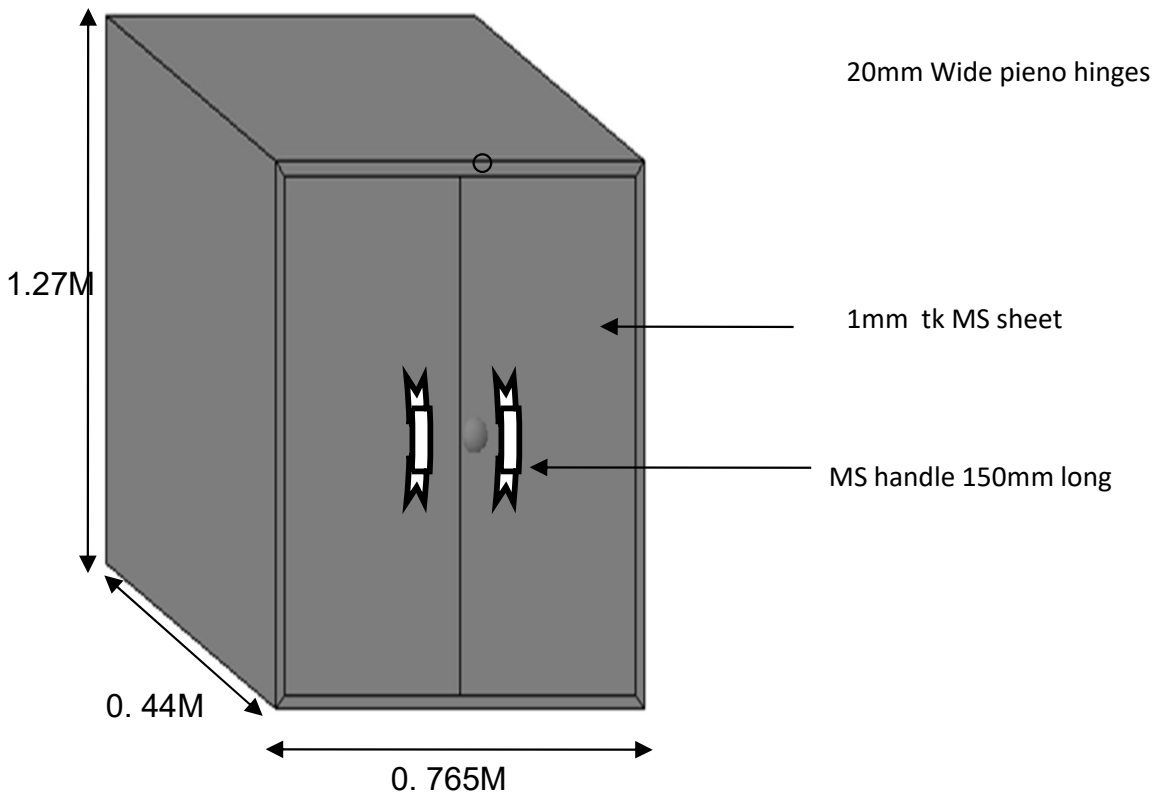


MS CABINET

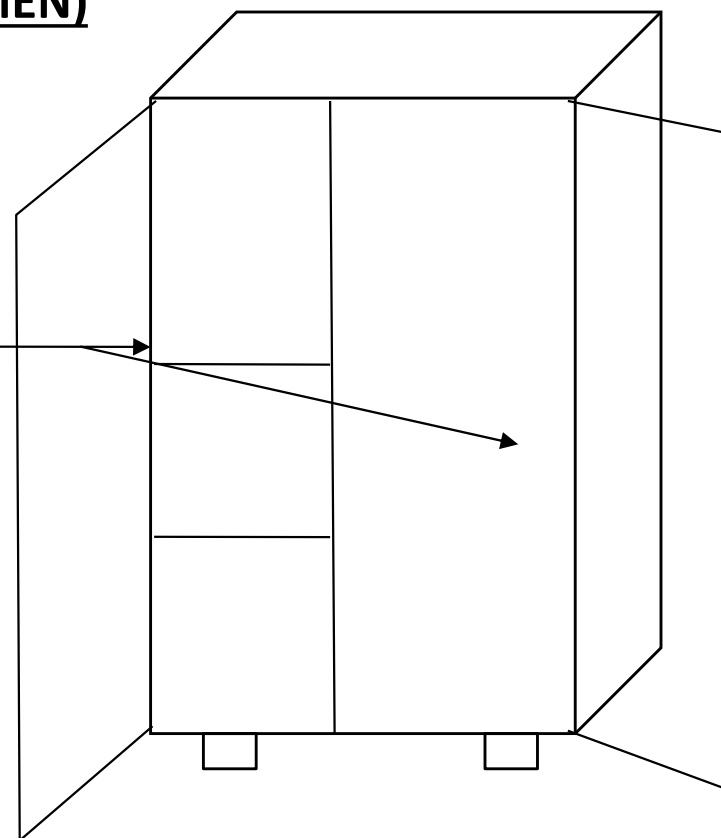

LIVING SHELTER (06 MEN)	
JOB NO : OT/NC/16/CIF(R)/2026-27/6616	
SCALE : NTS	SHEET NO : 01/09
DATE : 2026	UNIT : 8 ENGR REGT
EPO	CO


LIVING SHELTER (MLS 06 MEN)

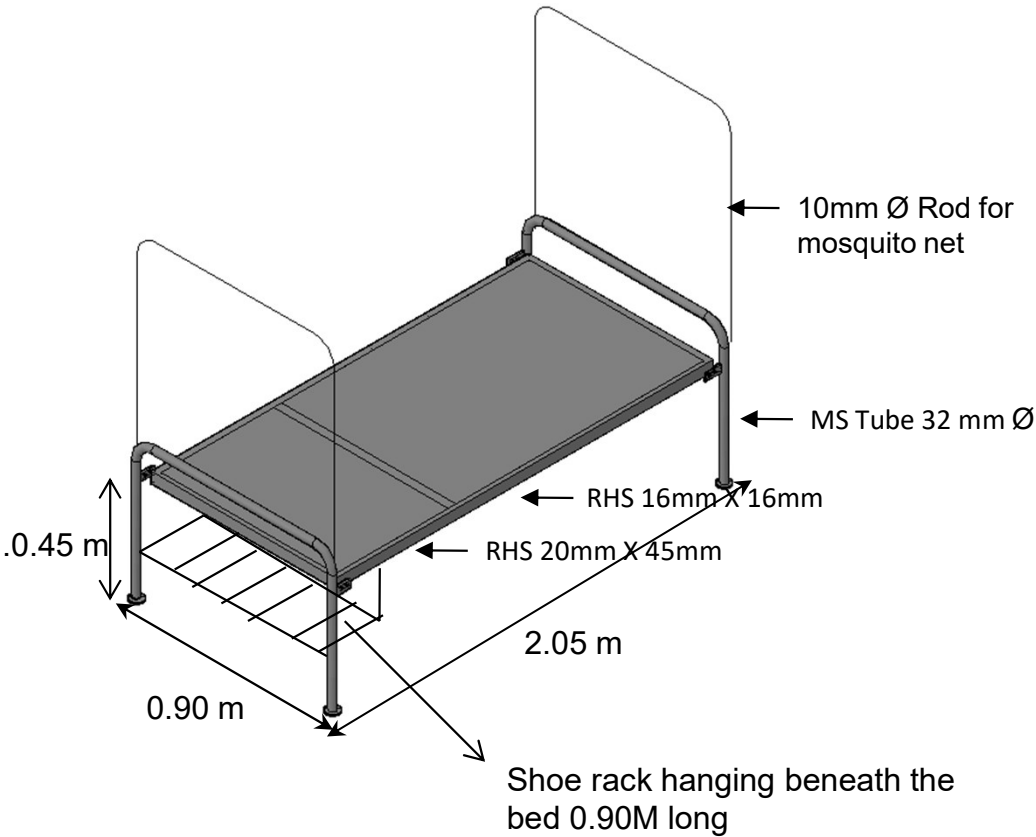

**SINGLE BUNK BED
WITH SHOE RACK**

LIVING SHELTER (06 MEN)	
JOB NO : OT/NC/16/CIF(R)/2026-27/6616	
SCALE : NTS	SHEET NO : 01/09
DATE : 2026	UNIT : 8 ENGR REGT
EPO	CO

STEEL DOUBLE BUNK

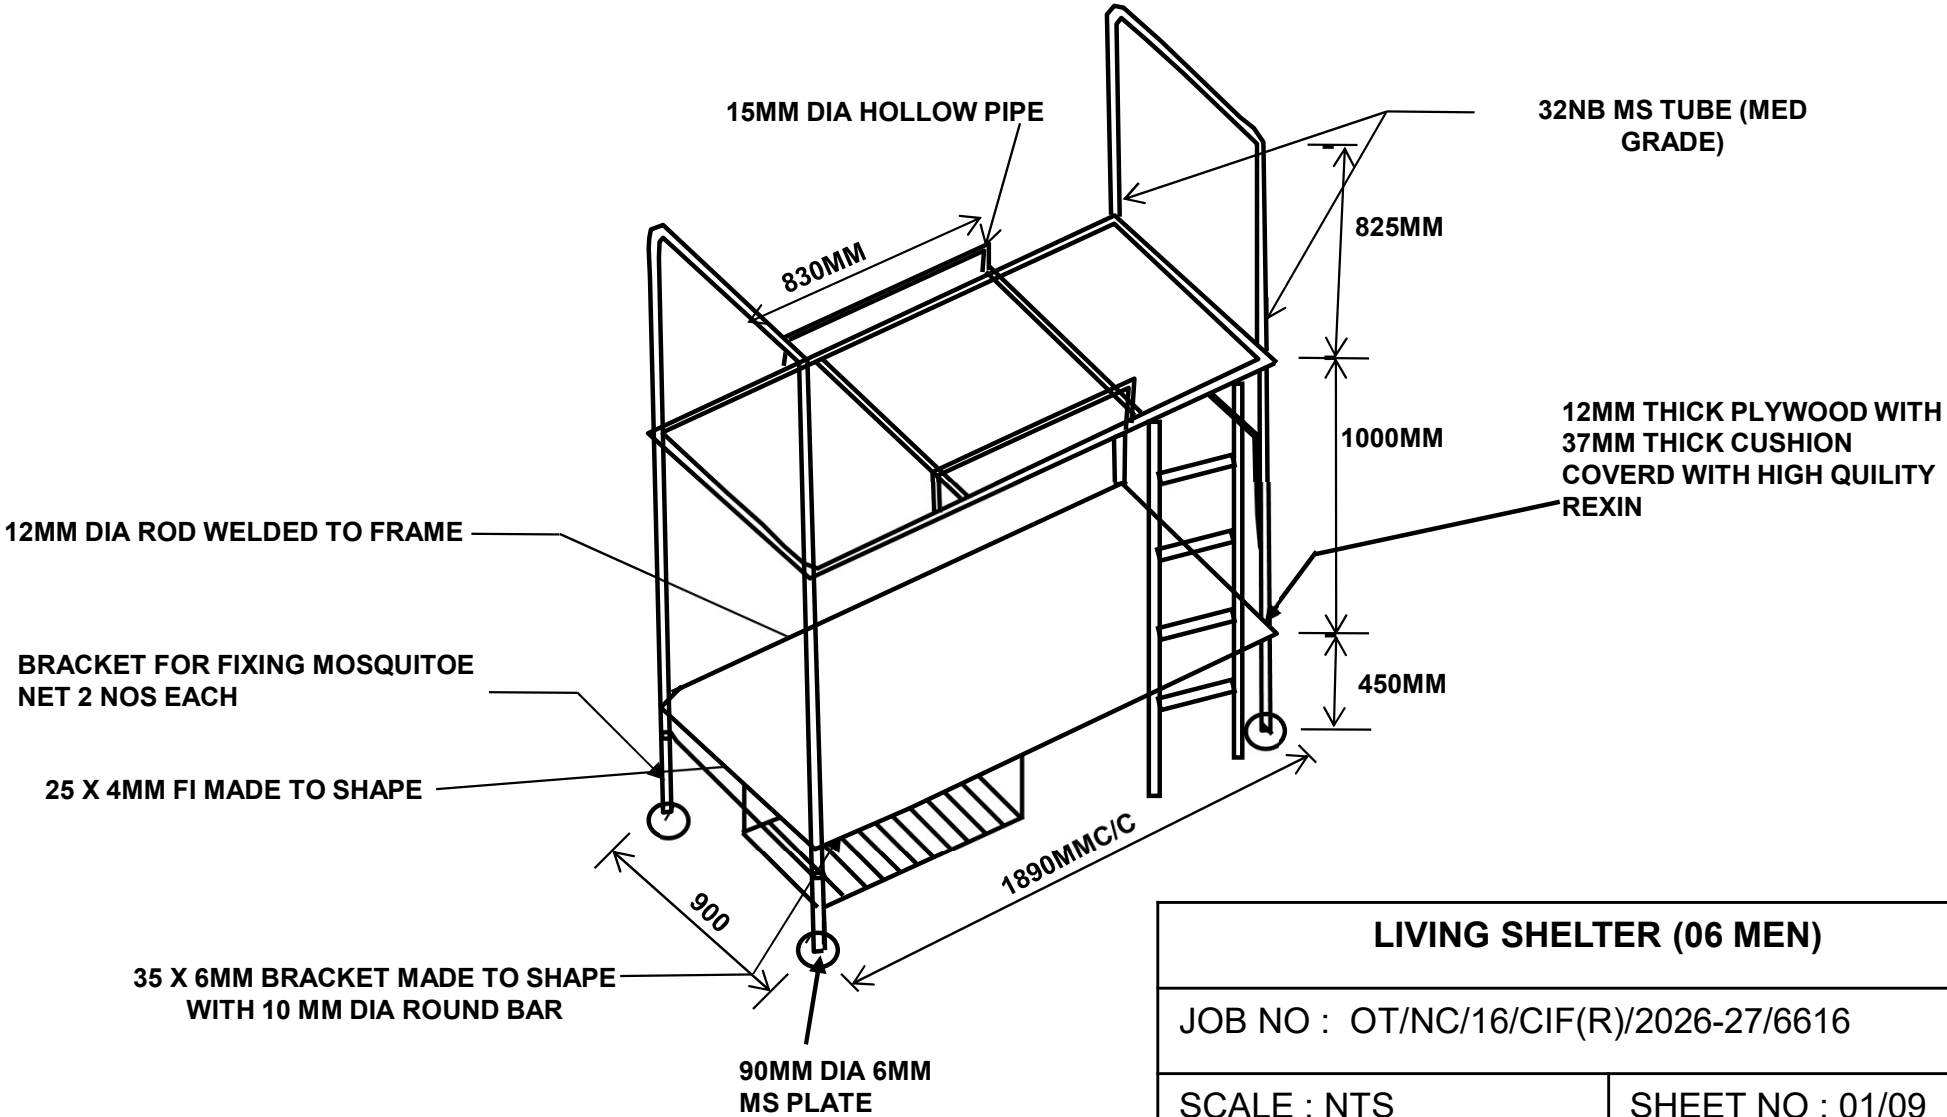

LIVING SHELTER (06 MEN)	
JOB NO : OT/NC/16/CIF(R)/2026-27/6616	
SCALE : NTS	SHEET NO : 01/09
DATE : 2026	UNIT : 8 ENGR REGT
EPO	CO